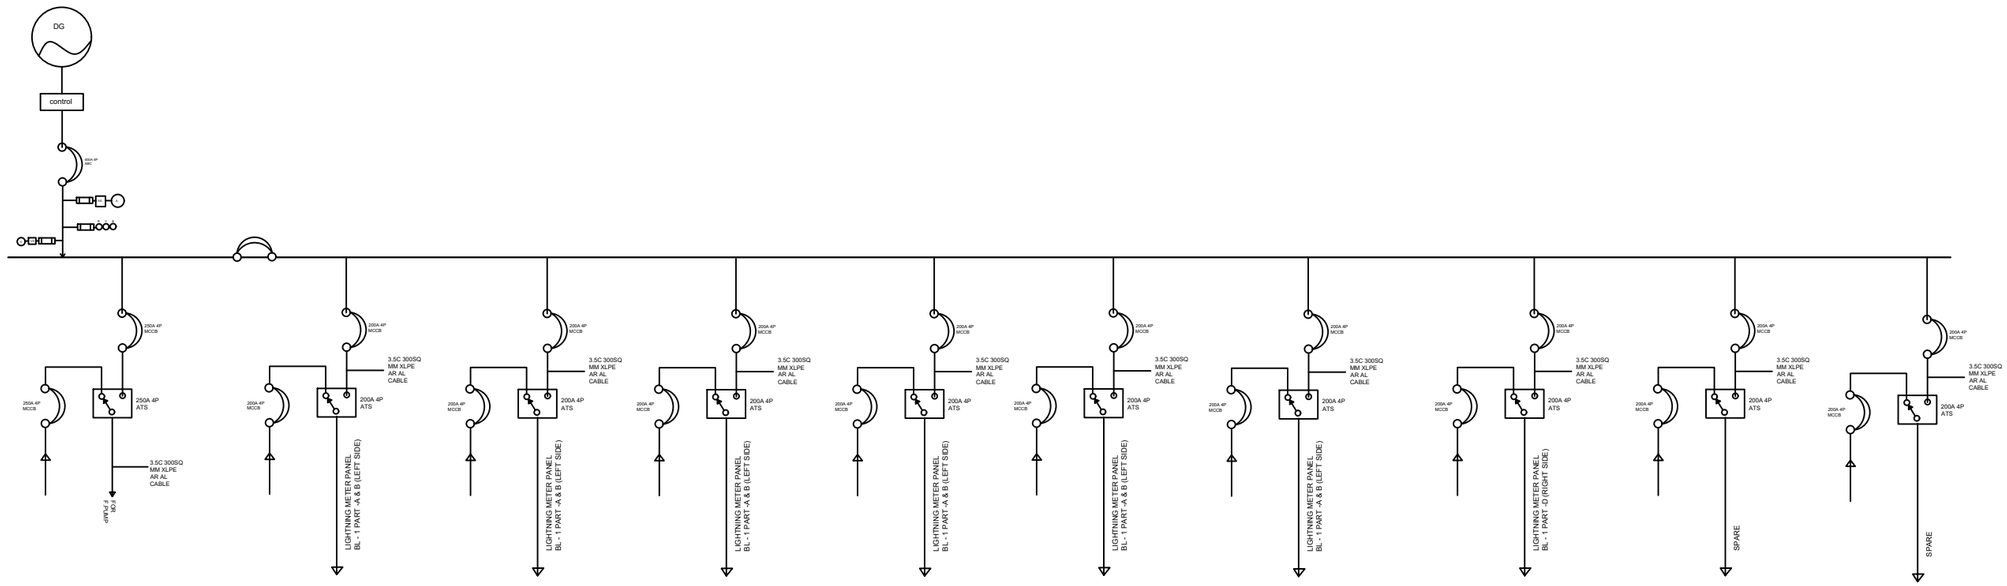



Project: Commercial Emergency Distribution

Drawing: Standby DG & ATS SLD

Drawn By: Julio Tito

Sheet: E-101